


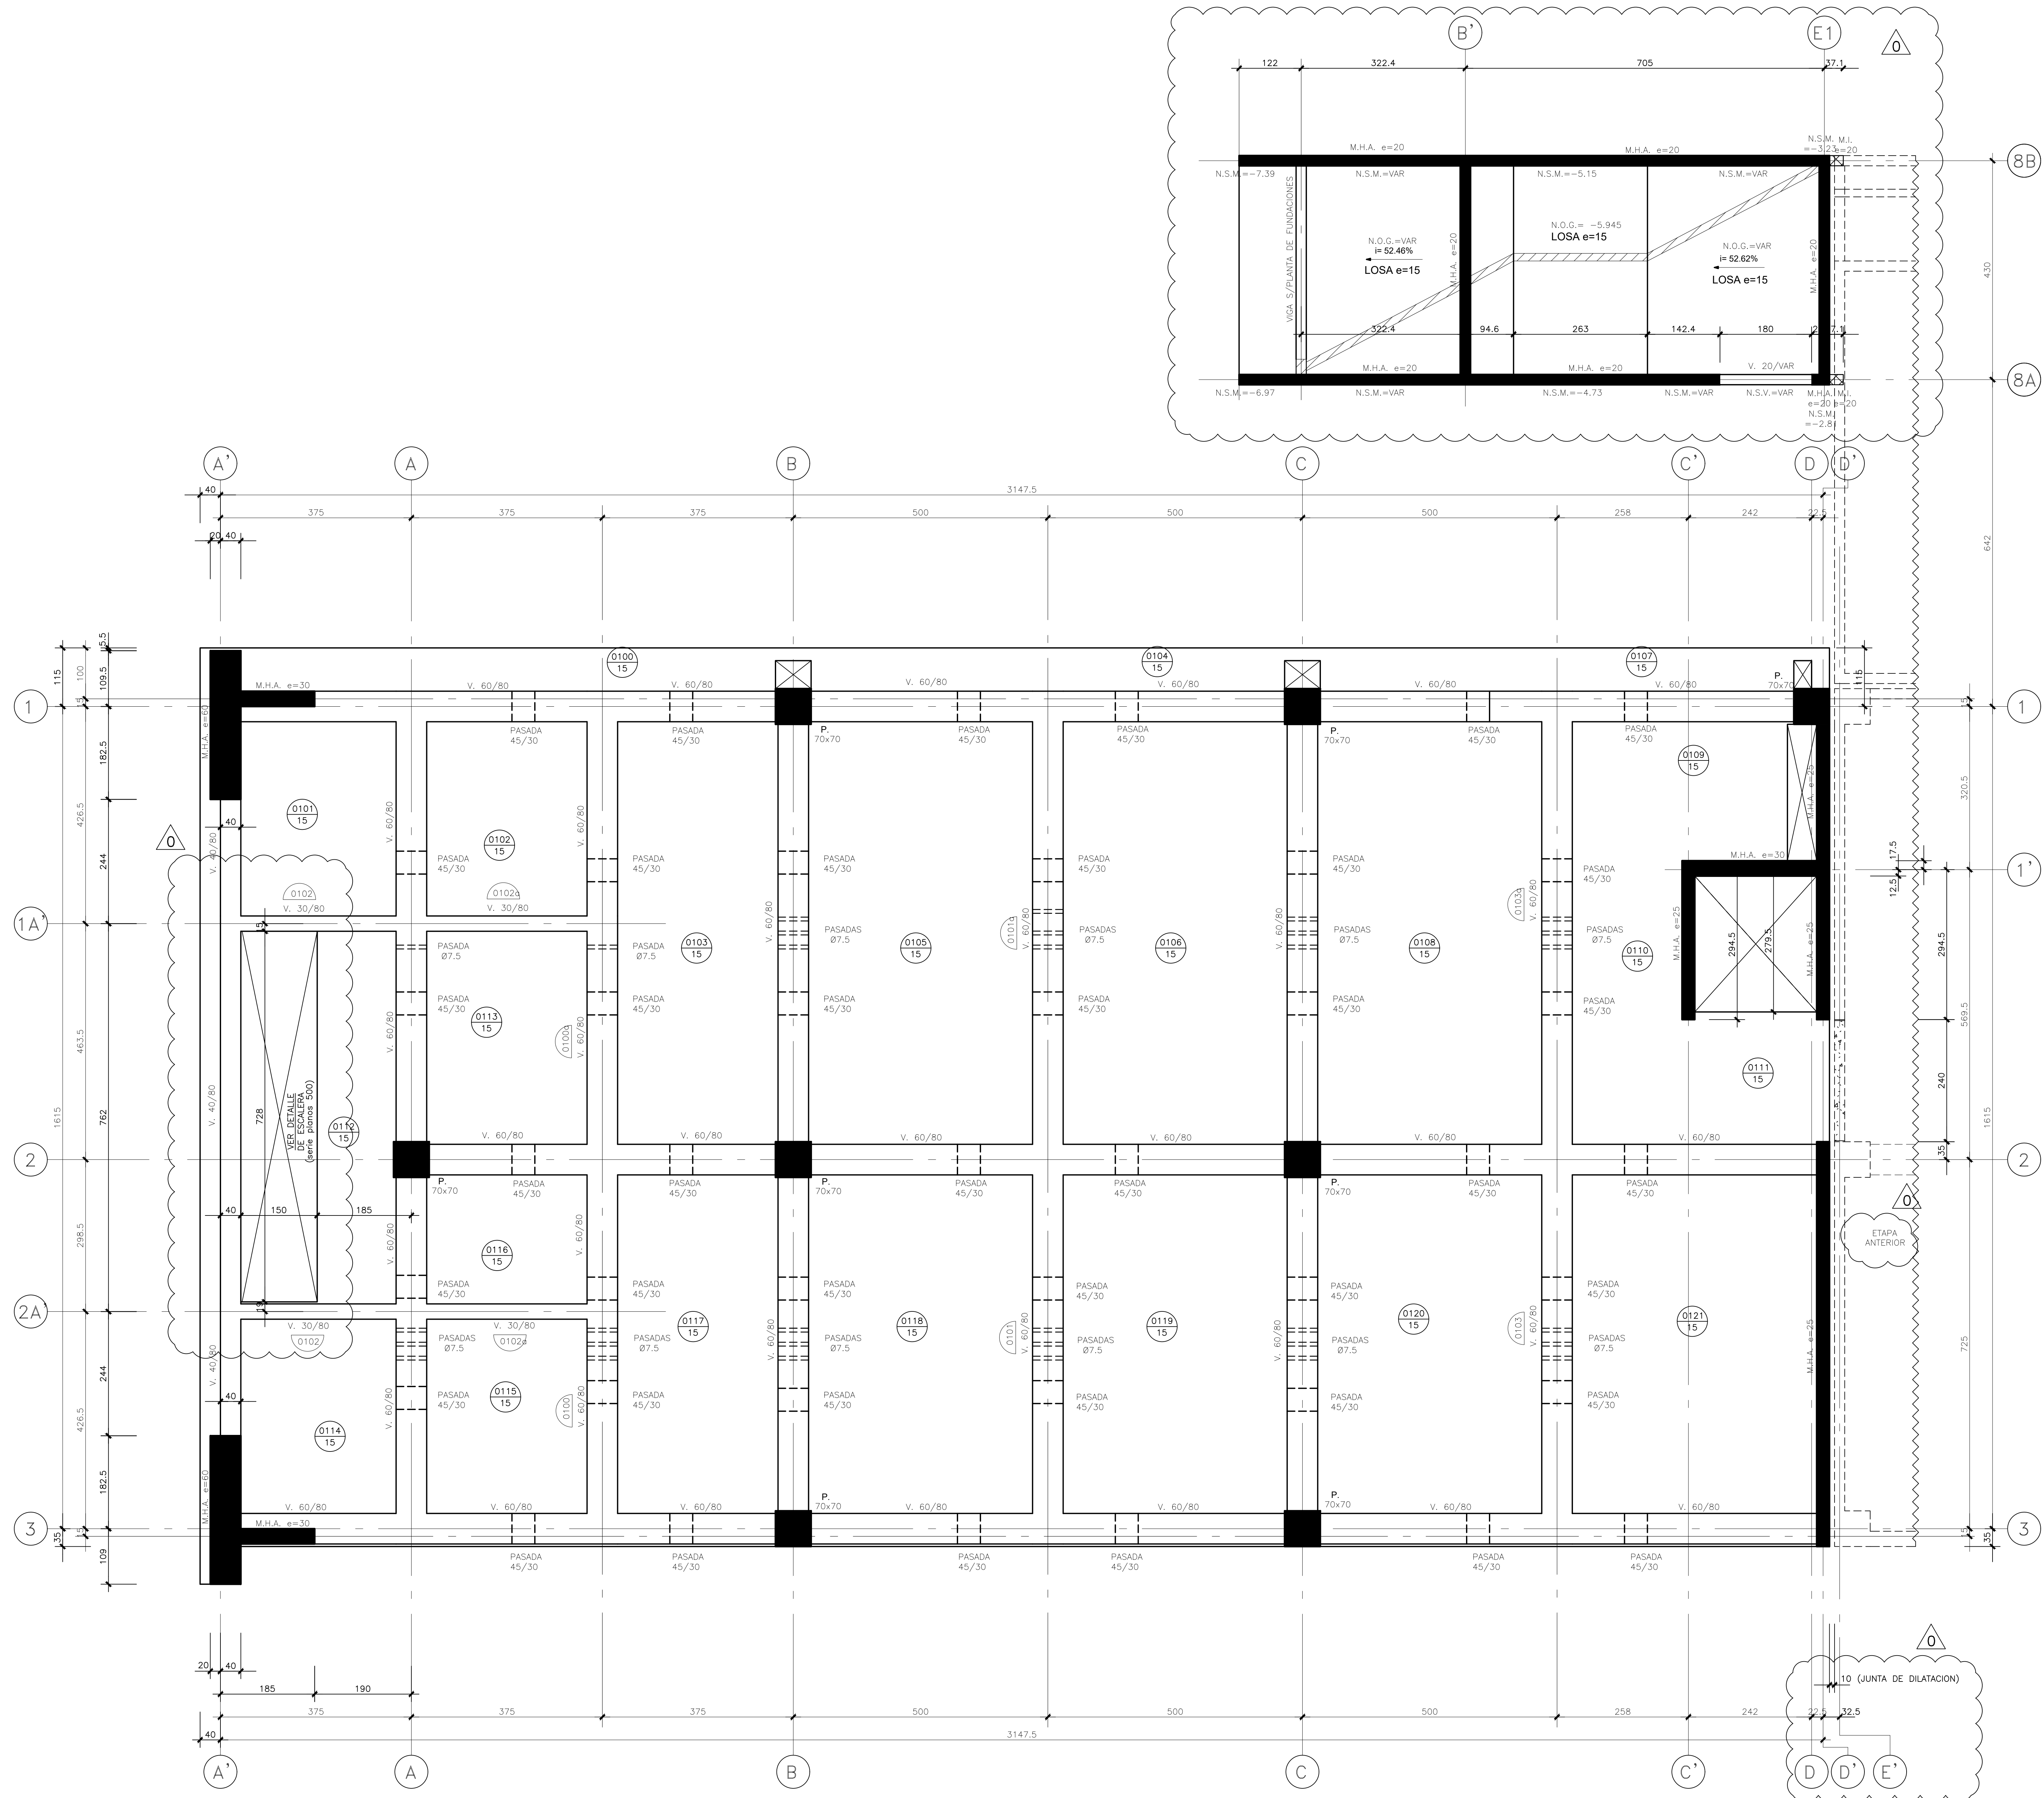

LOSA e=15
NIVEL SUPERIOR LOSA S/CUADRO (S.I.C.)
PLANTA CIELO 1°SUBTERRANEO a CIELO PISO 3°
ESCALA 1:50

CUADRO DE NIVELES	
CIELO PISO	NIVEL
1°S	-4.01
1°	-0.05
2°	+3.91
3°	+7.87

CUADRO DE CONTRAFLECHAS	
LOSA	CONTRAFLECHA (cm.)
0100	-
0101	-
0102	-
0103	-
0104	-
0105	0.5
0106	0.5
0107	-
0108	0.5
0109	-
0110	-
0111	-
0112	0.5
0113	-
0114	-
0115	-
0116	-
0117	-
0118	0.5
0119	0.5
0120	0.5
0121	0.5

NOTA: LOS ELEMENTOS ESTRUCTURALES DEBERÁN CONSIDERARSE CENTRADOS RESPECTO DE SU EJE EN PLANTA, SALVO INDICACIÓN EXPLÍCITA.

ESTADO:		APROBADO PARA:	
EN DESARROLLO	PRELIMINAR	PROPUESTA	CONSTRUCCION X
REVISION		ING. / DIB.	FECHA
SE EMITE PARA CONSTRUCCION		MKC/ARB	24/10/2024
PROYECTO		U. DE LOS ANDES (FASE 2)	
CONTENIDO		PLANTA CIELO 1°SUBTERRANEO a CIELO PISO 3°	
CALCULO		DIBUJO	NUMERO
M. KUPFER C.		A. ROCHA B.	2024_22-101
REVISOR		FECHA	
A. ROCHA B.		OCTUBRE 2024	

FIRMA REVISOR INDEPENDIENTE CALCULO

FIRMA ING. RESPONSABLE

ISO 9001

FONO: +56 2 25941300
info@renelagos.com
www.renelagos.com

renelagos
engineers

REN LAGO CONTRERAS
INGENIERO CIVIL
INGENIERO EN SISTEMAS DE AGUA
LUGAR DE LA FUENTE MARTINEZ
SINCE SANJUAN TORREAN

PROYECTO

CONTENIDO

CALCULO

DIBUJO

REVISOR

FECHA

NUMERO