

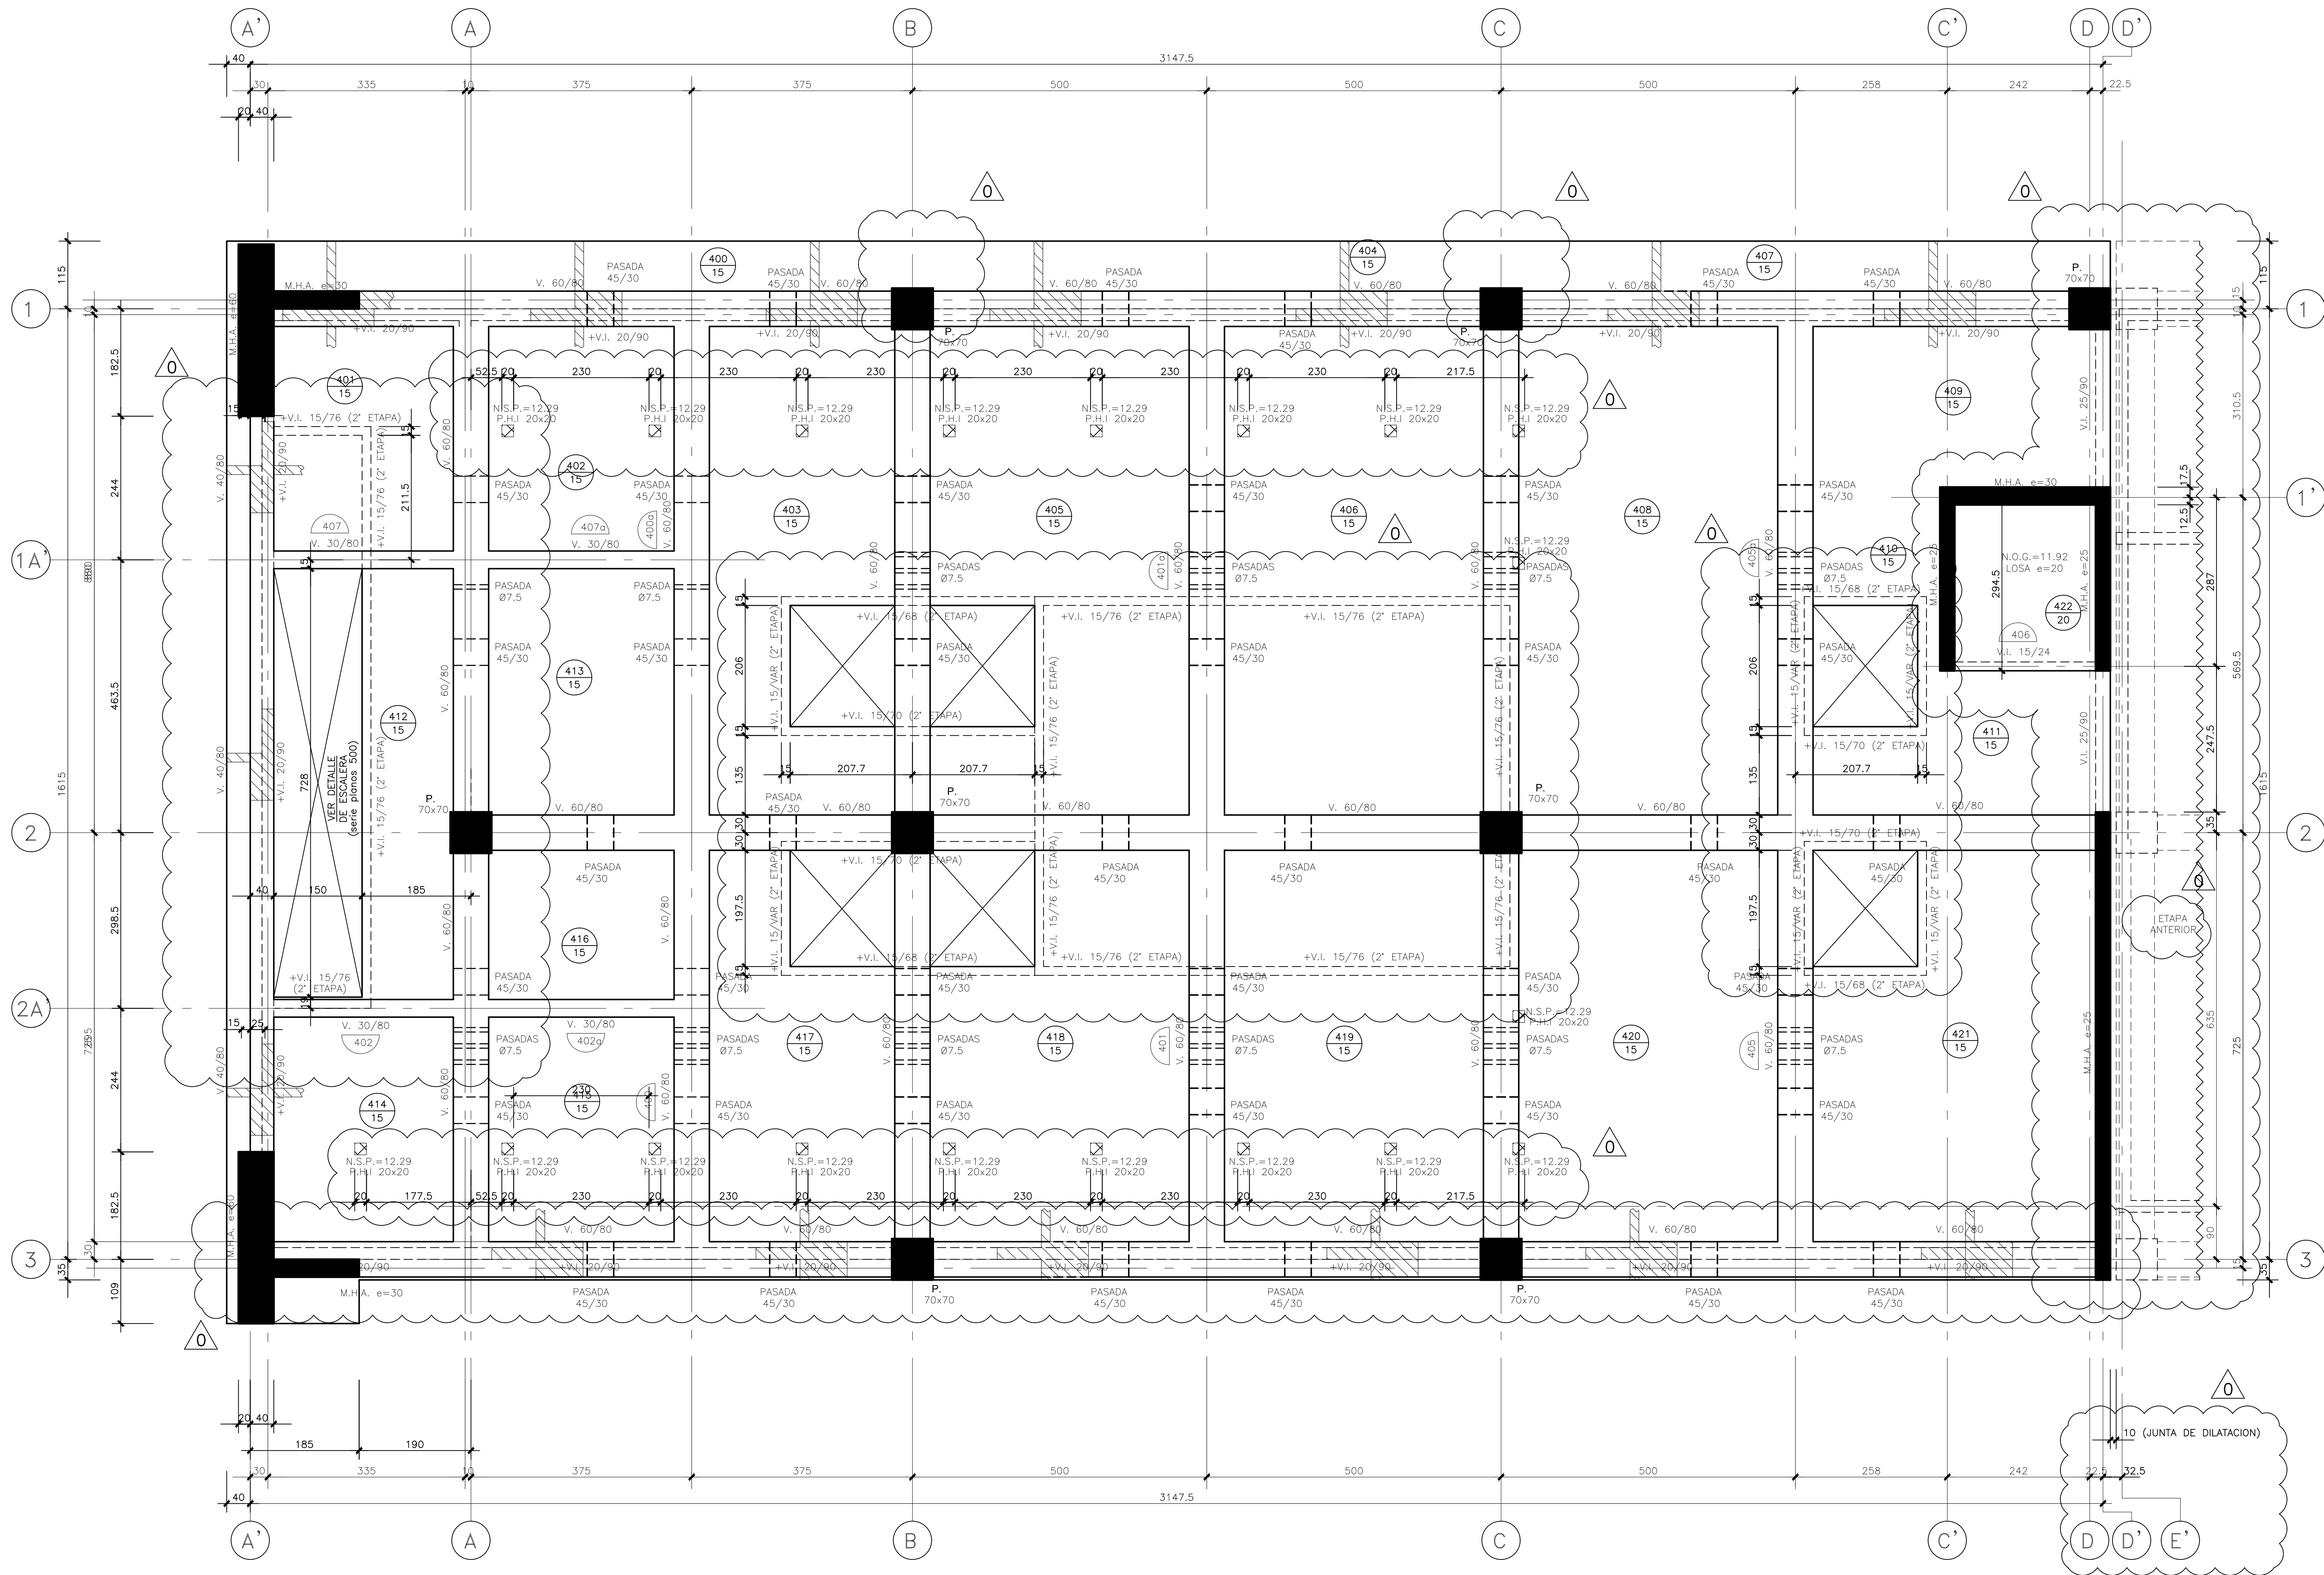


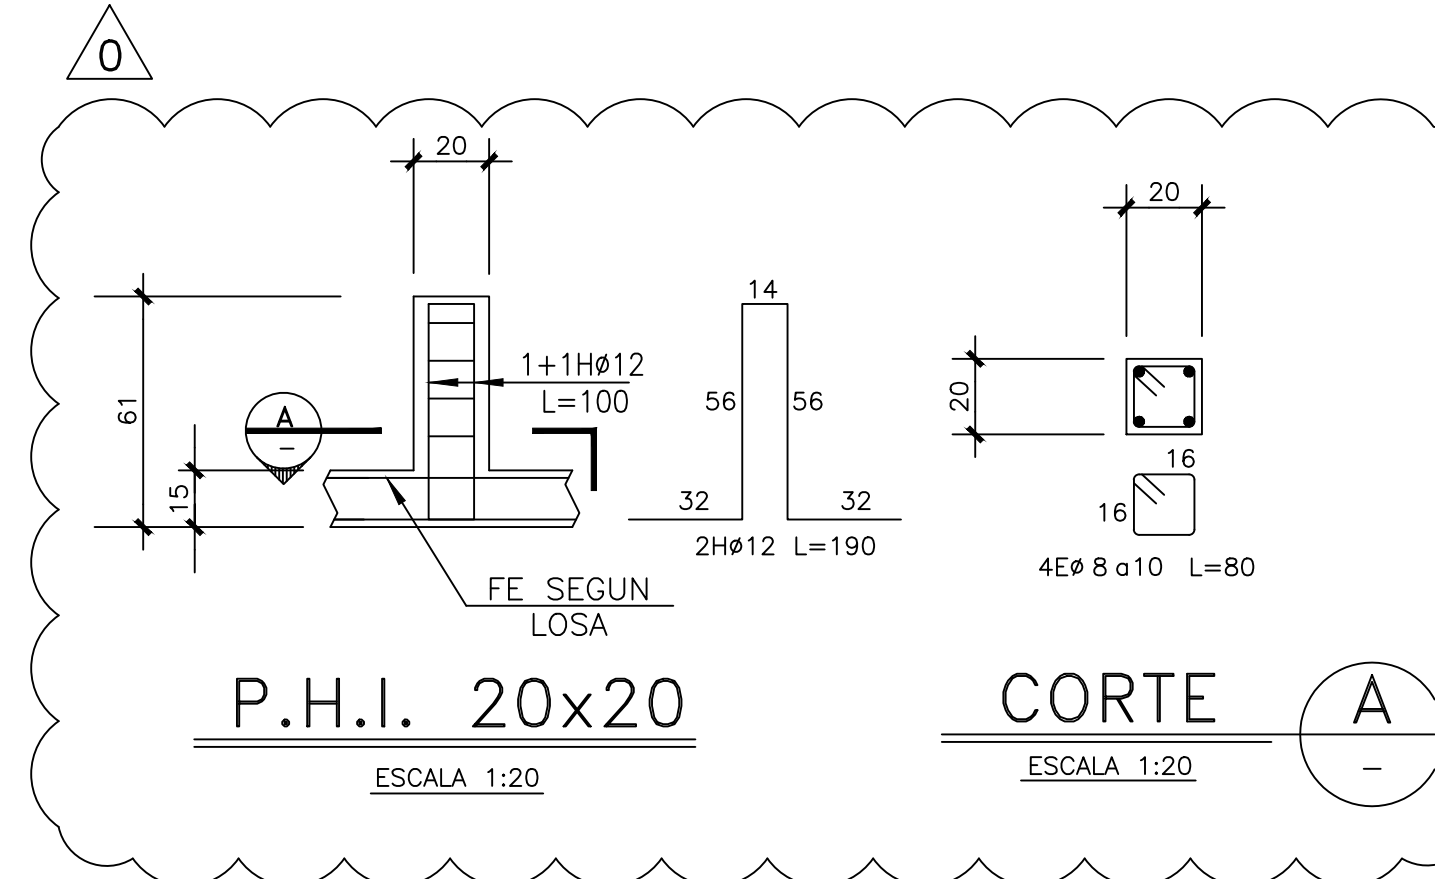

LOSA e=15
(NIVEL SUPERIOR LOSA + 11.83)
PLANTA CIELO 4º PISO
ESCALA 1:50

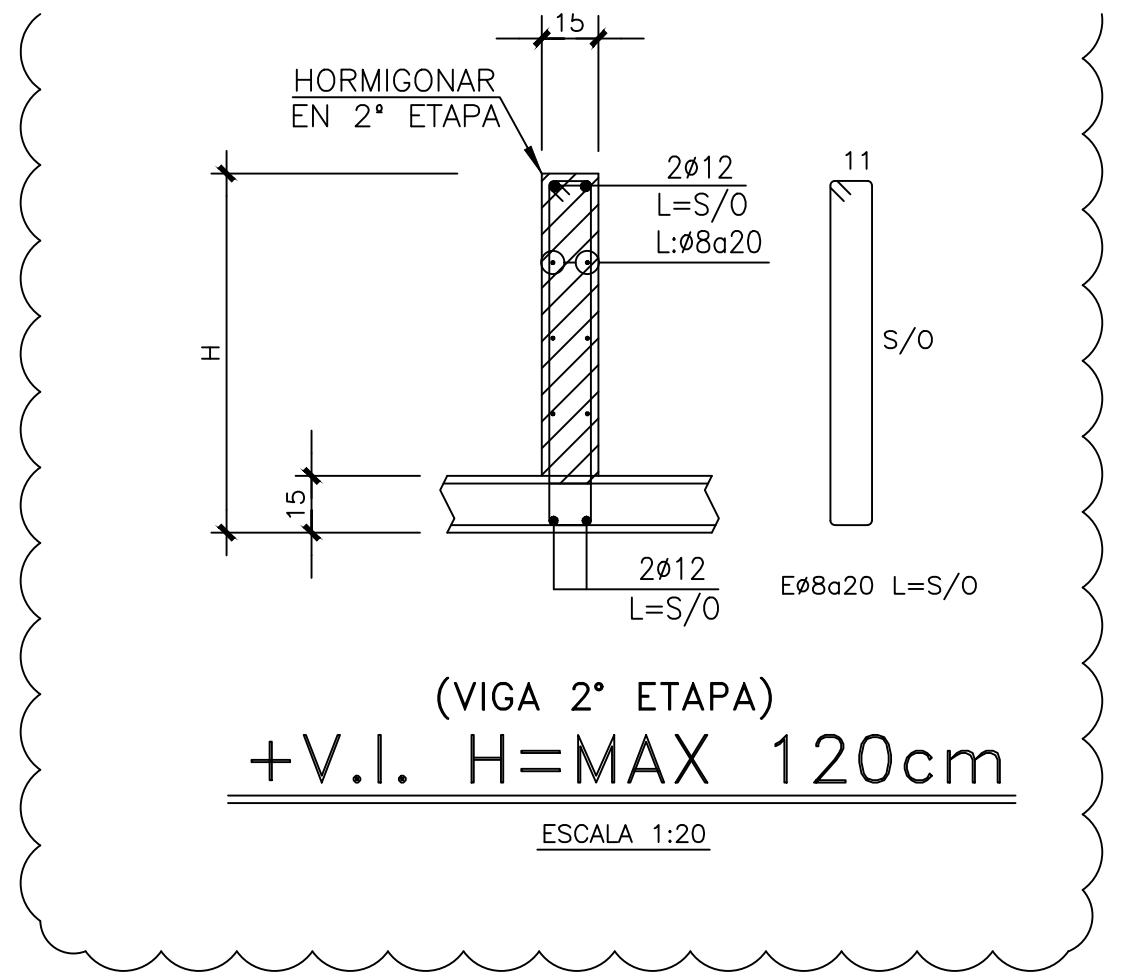

CUADRO DE CONTRAFLECHAS	
LOSA	CONTRAFLECHA (cm.)
400	-
401	-
402	-
403	-
404	-
405	0.5
406	0.5
407	-
408	0.5
409	-
410	-
411	-
412	0.5
413	-
414	-
415	-
416	-
417	-
418	0.5
419	0.5
420	0.5
421	0.5

NOTA: LOS ELEMENTOS ESTRUCTURALES DEBERÁN CONSIDERARSE CENTRADOS RESPECTO DE SU EJE EN PLANT SALVO INDICACIÓN EXPLÍCITA.